




Stantec Consulting Michigan Inc.
3959 Research Park Drive
Ann Arbor, Michigan
48108-2216
Tel. 734.761.1010
Fax. 734.761.1200
www.stantec.com

Stantec

Copyright Reserved

The Contractor shall verify and be responsible for all dimensions. DO NOT scale the drawing - any errors or omissions shall be reported to Stantec without delay.
The Copyrights to all designs and drawings are the property of Stantec. Reproduction or use for any purpose other than that authorized by Stantec is forbidden.

Consultants

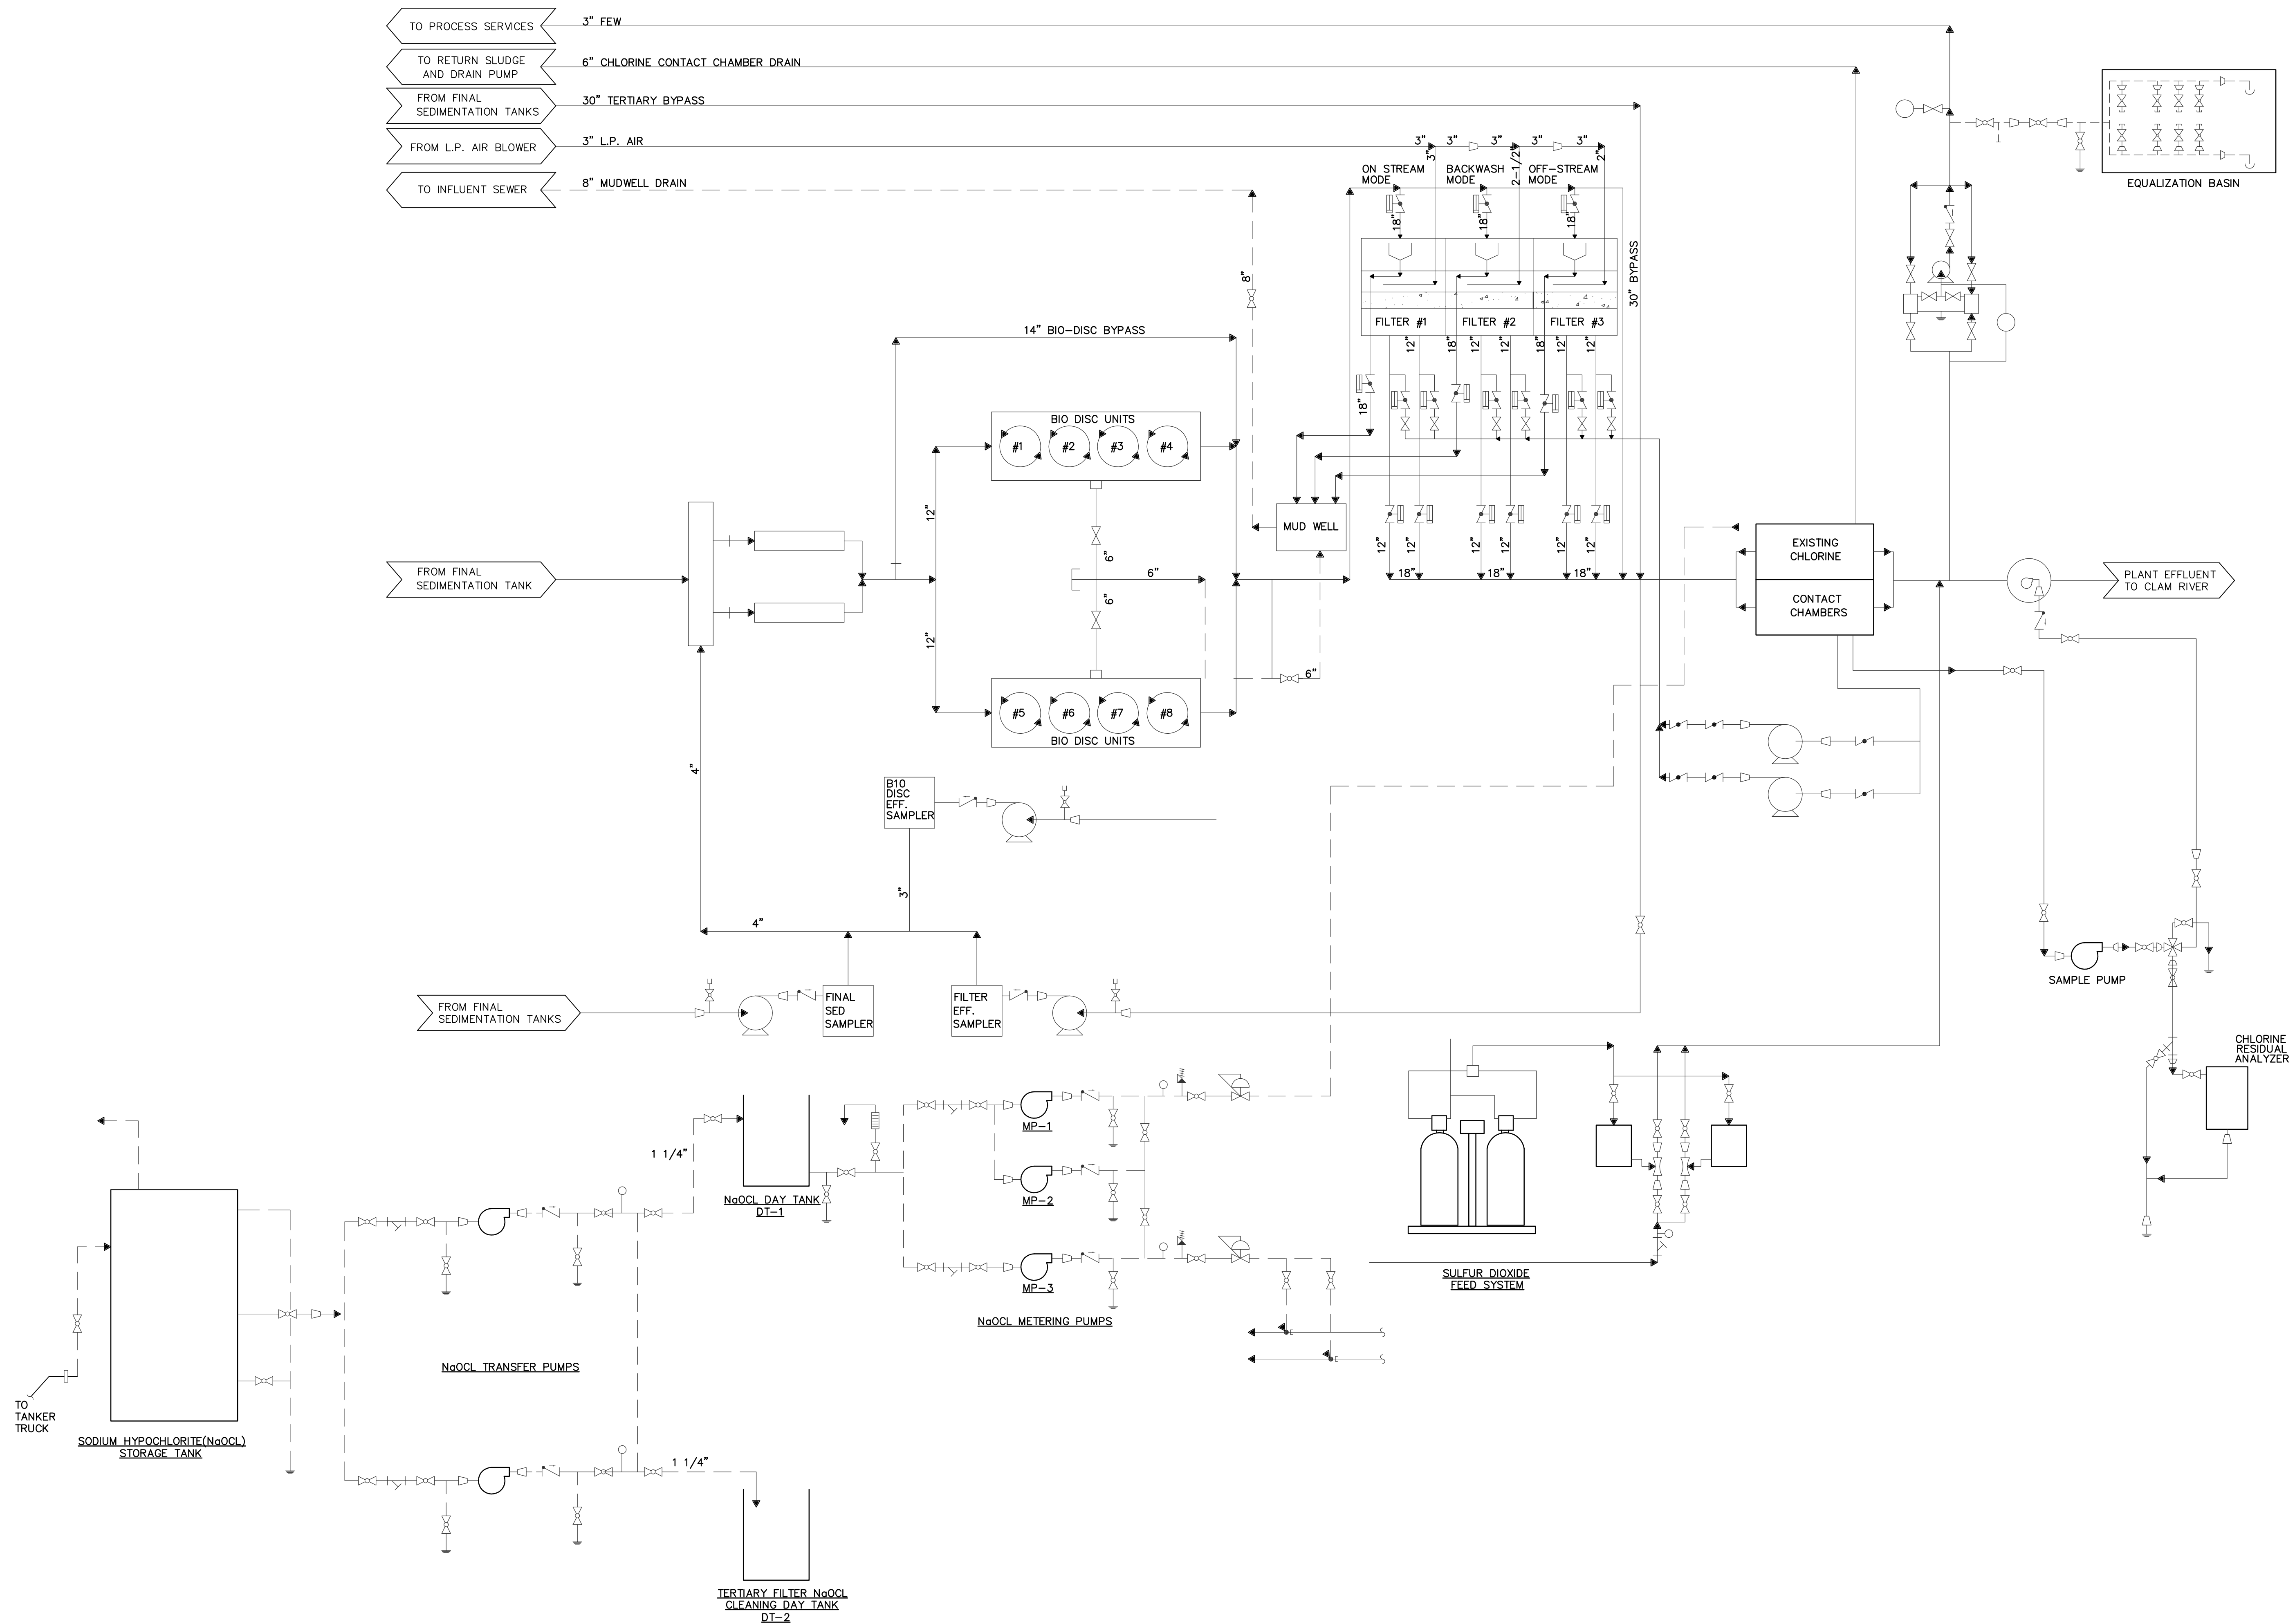

Revision	By	Appd.	YY.MM.DD
MDEQ PERMIT	WA	IMN	07.03.02
Issued	By	Appd.	YY.MM.DD
File Name: DP1-01 ProcessFlow	JLP	IMN	WA
	Dwn.	Chkd.	Dsgn.
Permit-Seal			YY.MM.DD

Client/Project

CITY OF CADILLAC, MICHIGAN
WASTEWATER TREATMENT PLANT
2007 IMPROVEMENTS

CADILLAC, MI

Title

PROCESS FLOW
DIAGRAM I

Project No.

2075006103

Scale

AS NOTED

Drawing No.

Sheet

Revision

OP1.01

- of