



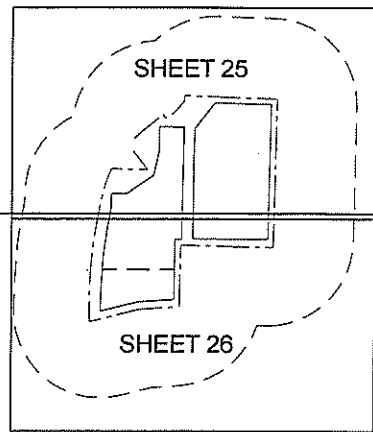

MAP KEY
NOT TO SCALE

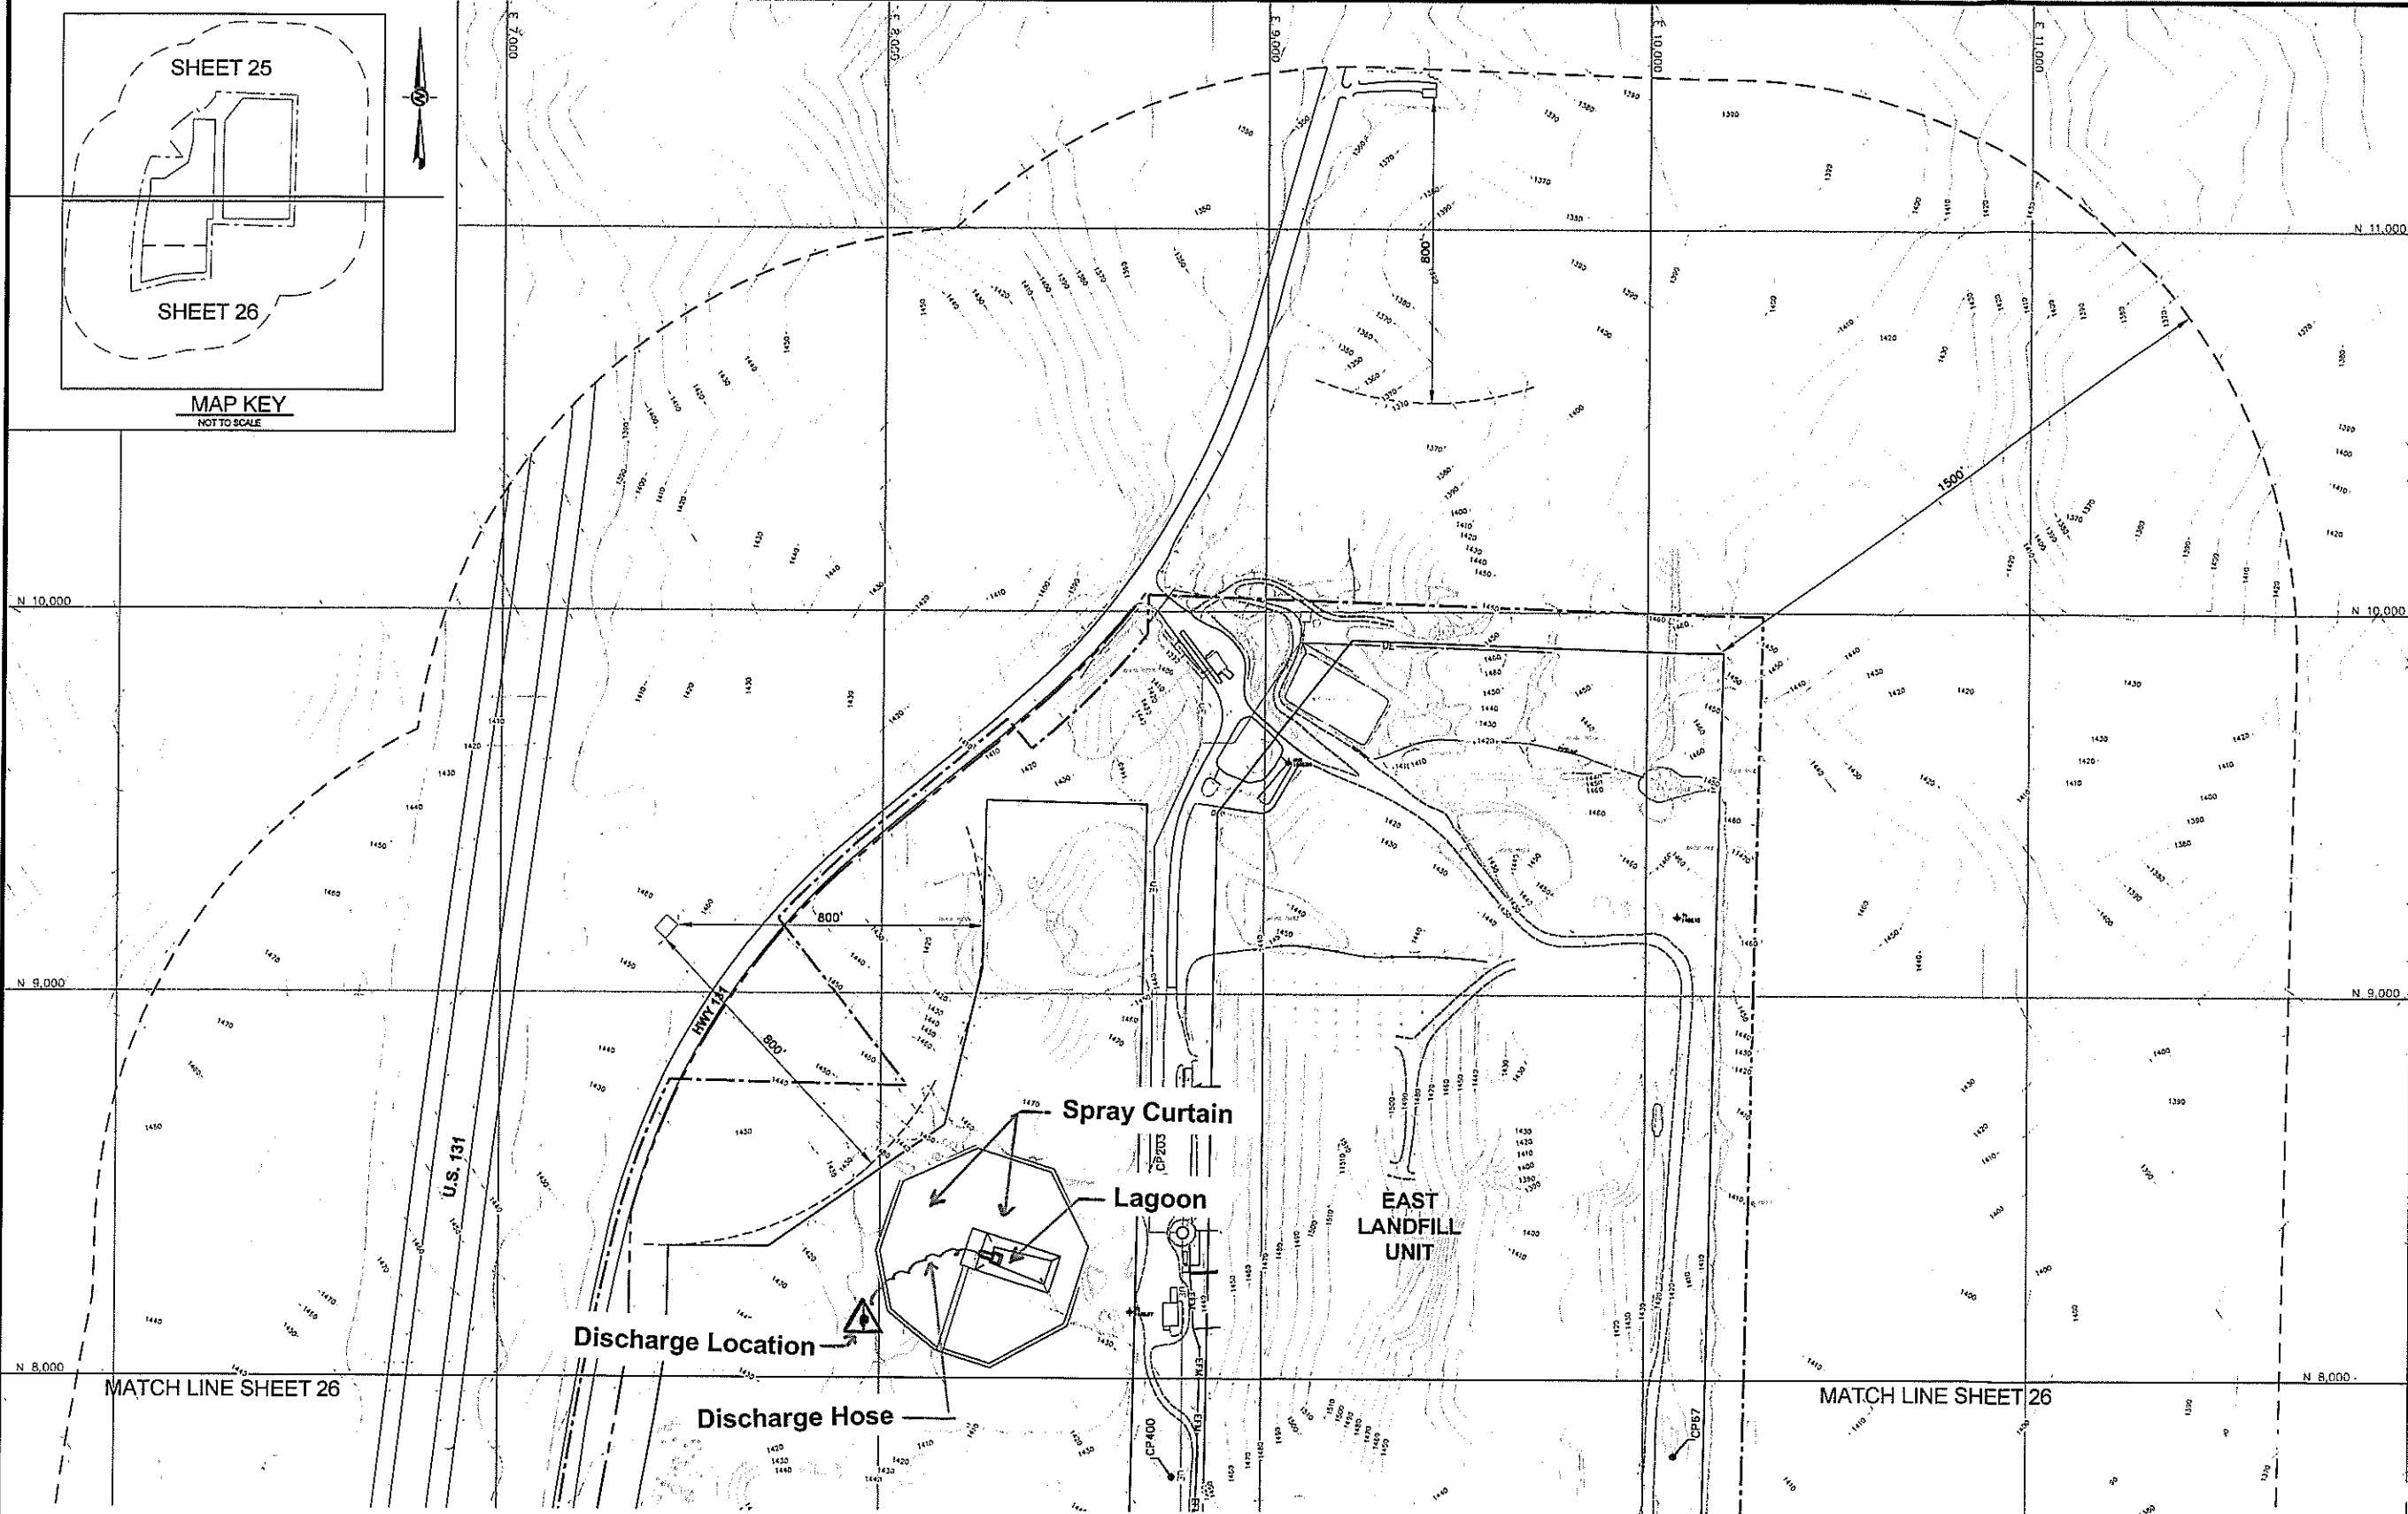

LEGEND

- LANDFILL PROPERTY BOUNDARY
- ROAD RIGHT-OF-WAY
- EXISTING APPROVED CELL BOUNDARY
- PROPOSED SOLID WASTE BOUNDARY
- PROPOSED CELL BOUNDARY
- EXISTING GRADES
- PROPOSED GRADES
- PAVED ROAD
- UNPAVED ROAD

NOTES

- THE TOPOGRAPHIC MAP WAS PREPARED BY ADVANCE MAPPING TECHNOLOGIES INC., TRAVERSE CITY, MI. DATE OF AERIAL PHOTOGRAPHY APRIL 27, 2008, AND ON-SITE SURVEYS, MOST RECENTLY DATED MARCH 9, 2011. ADDITIONAL TOPO SHOWN BEYOND AERIAL TOPOGRAPHY WAS TAKEN FROM GOOGLE EARTH PRO.
- HORIZONTAL GRID SYSTEM IS BASED ON A SITE SPECIFIC LOCAL GRID.
- VERTICAL DATUM IS BASED ON MEAN SEA LEVEL.
- RESIDENCE LOCATIONS APPROXIMATED FROM AERIAL PHOTOGRAPH, APRIL 27, 2008 ADVANCE MAPPING TECHNOLOGIES, INC. AND GOOGLE EARTH PRO.



WEXFORD COUNTY
LANDFILL, LLC
MANTON, MICHIGAN

TOPOGRAPHIC MAP

PROJECT No. 123-88763		
FILE No. 12388763A021-01		
SCALE AS SHOWN		
DESIGN	VRG	3/27/12
CADD	DJC	4/17/12
CHECK	PTS	4/18/12
REVIEW	VRG	4/19/12

5