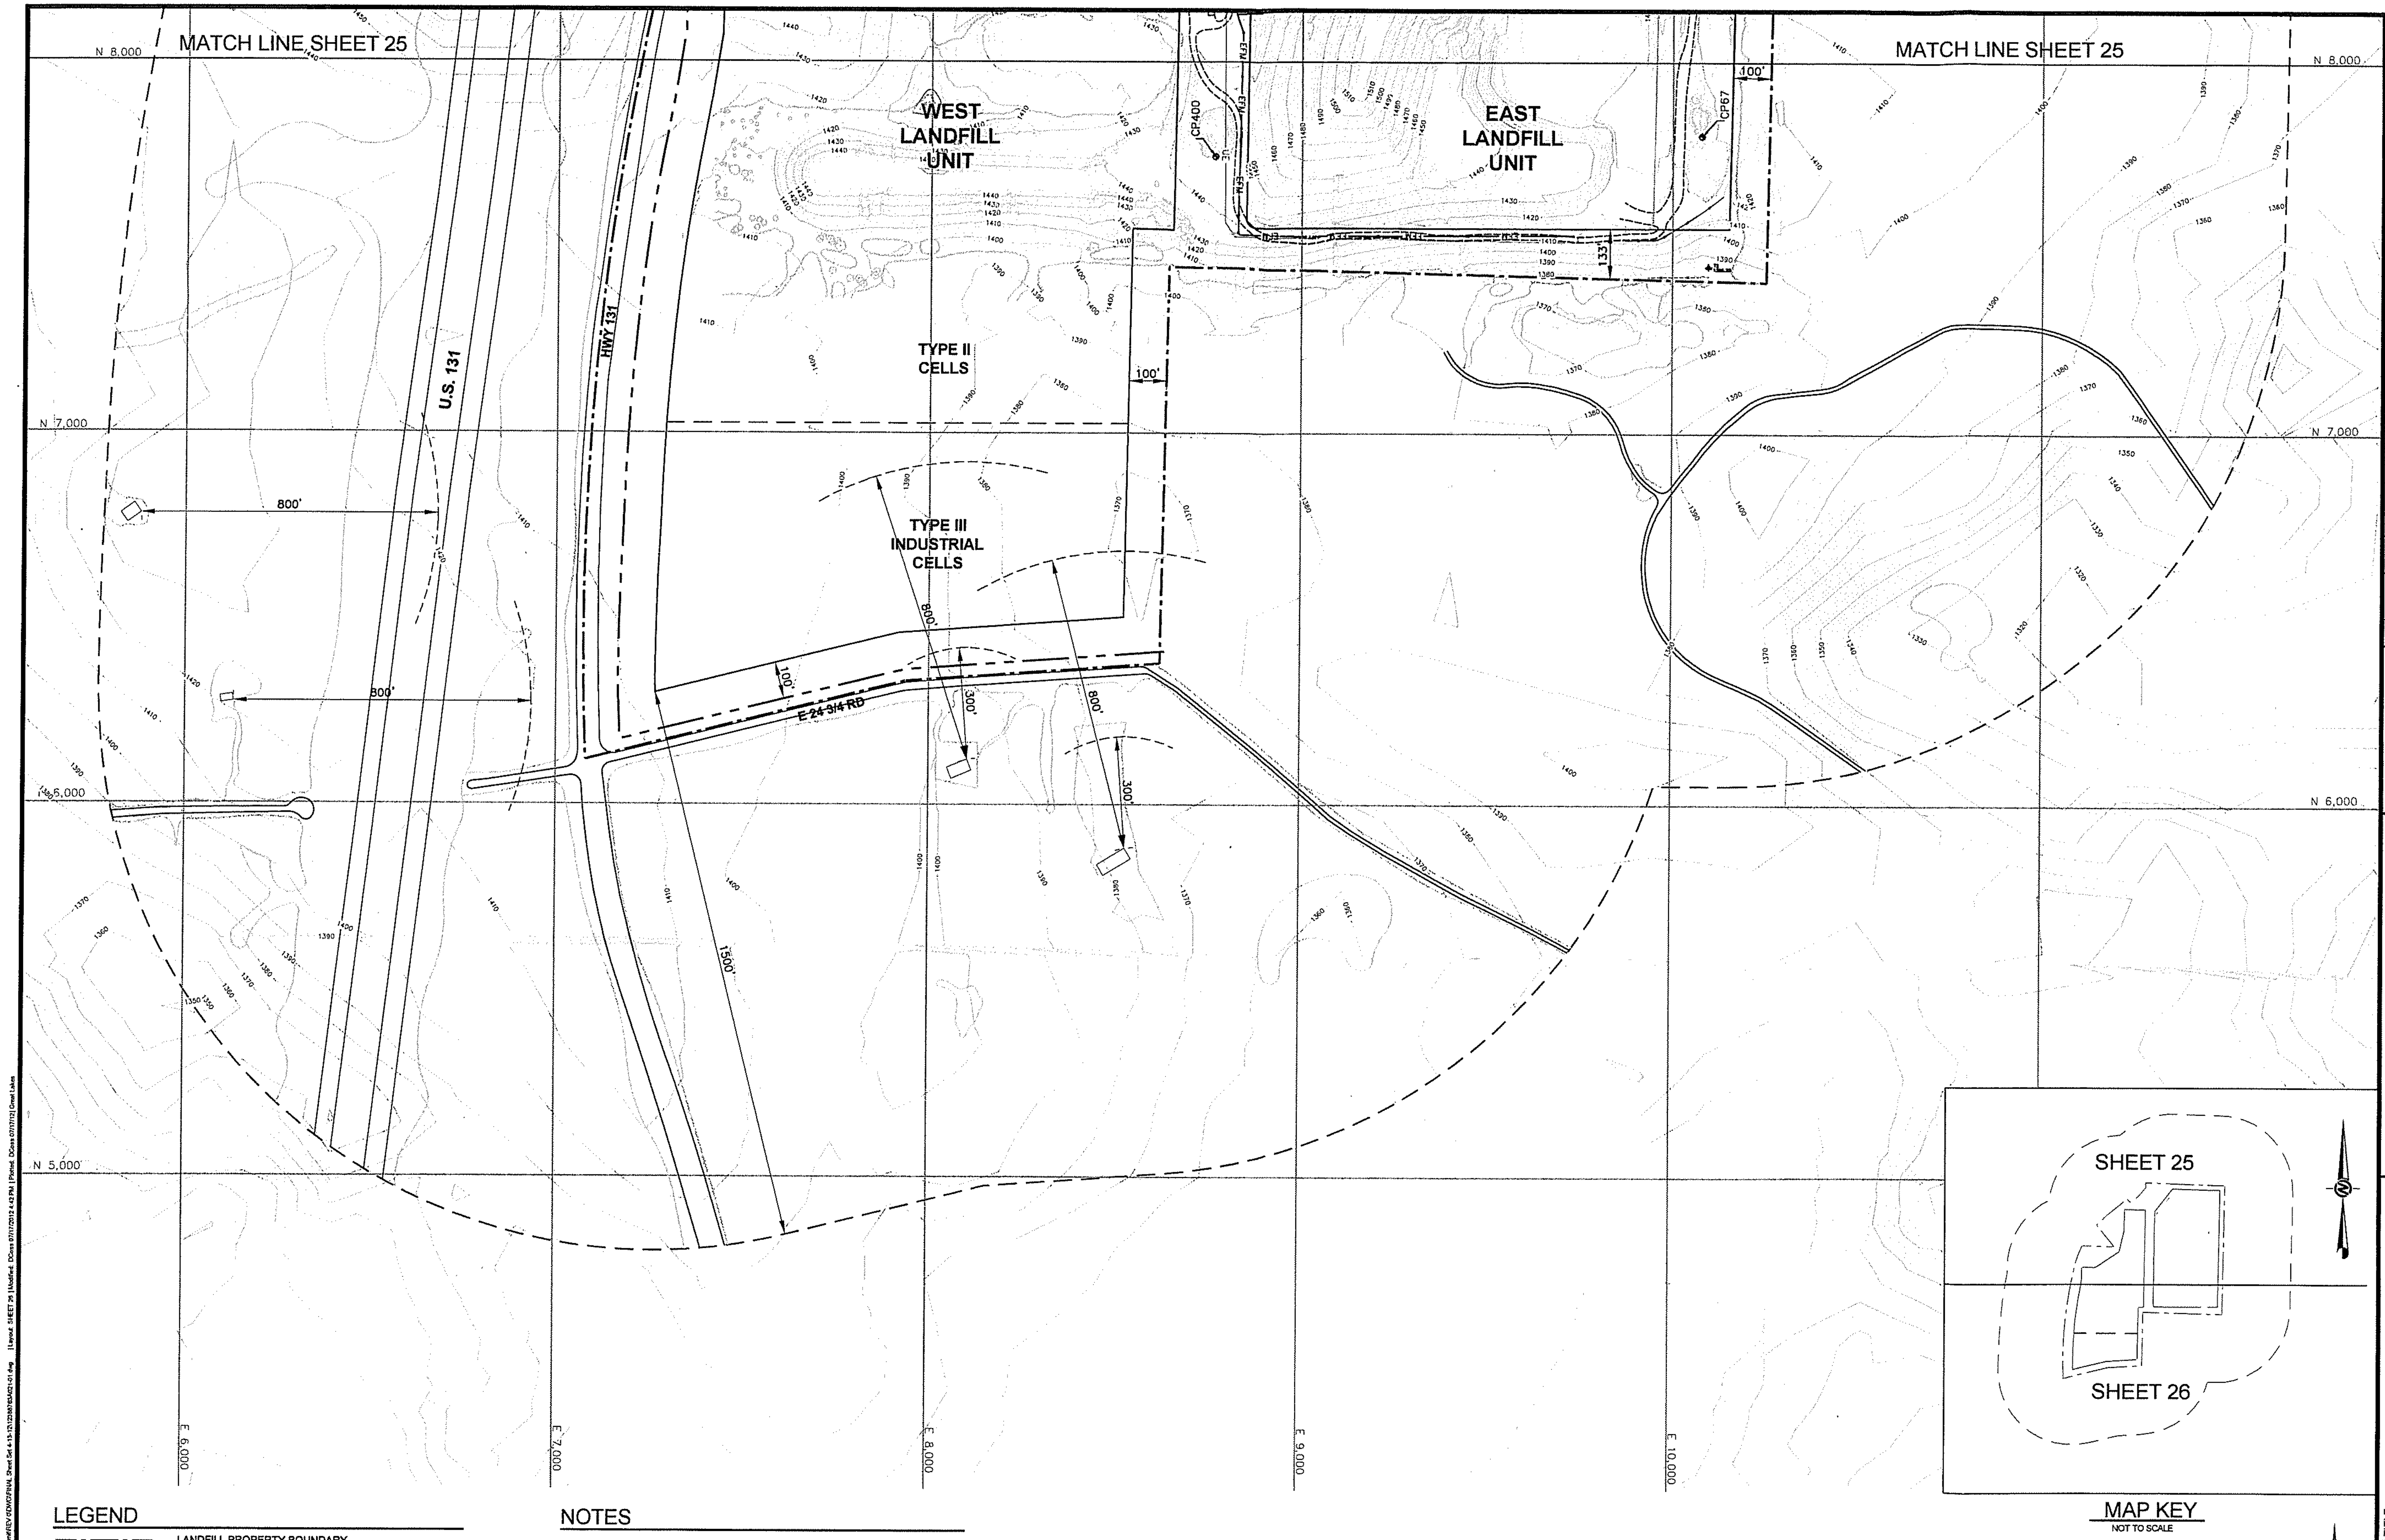

200 0 200 400
SCALE FEET

LEGEND

— - — - —	LANDFILL PROPERTY BOUNDARY
—— – – ——	ROAD RIGHT-OF-WAY
- - - - -	EXISTING APPROVED CELL BOUNDARY
———	PROPOSED SOLID WASTE BOUNDARY
— — — —	PROPOSED CELL BOUNDARY
1460	EXISTING GRADES
—1440—	PROPOSED GRADES
═══	PAVED ROAD
═ ═ ═	UNPAVED ROAD

NOTES

1. THE TOPOGRAPHIC MAP WAS PREPARED BY ADVANCE MAPPING TECHNOLOGIES INC., TRAVERSE CITY, MI. DATE OF AERIAL PHOTOGRAPHY APRIL 27, 2008, AND ON-SITE SURVEYS, MOST RECENTLY DATED MARCH 9, 2011. ADDITIONAL TOPO SHOWN BEYOND AERIAL TOPOGRAPHY WAS TAKEN FROM GOOGLE EARTH PRO.
2. HORIZONTAL GRID SYSTEM IS BASED ON A SITE SPECIFIC LOCAL GRID.
3. VERTICAL DATUM IS BASED ON MEAN SEA LEVEL
4. RESIDENCE LOCATIONS APPROXIMATED FROM AERIAL PHOTOGRAPH, APRIL 27, 2008 ADVANCED MAPPING TECHNOLOGIES, INC. AND GOOGLE EARTH PRO.

Golder Associates

REV	DATE	DES	REVISION DESCRIPTION	CADD	CHK	RVW
△	7/17/12	VRG	MDEQ COMMENTS	DJC	PTS	VRG

VICKI R GARON ENGINEER No. 38686

PROJECT

WEXFORD COUNTY
LANDFILL, LLC
MANTON, MICHIGAN

TITLE

TOPOGRAPHIC MAP

PROJECT No.		123-88763
FILE No.		12388763A021-01
SCALE		AS SHOWN
DESIGN	VRG	3/27/12
CADD	DJC	4/17/12
CHECK	PTS	4/18/12
REVIEW	VRG	4/18/12

6