




Copyright Reserved

The Contractor shall verify and be responsible for all dimensions. DO NOT scale the drawing – any errors or omissions shall be reported to Stantec without delay.

The Copyrights to all designs and drawings are the property of Stantec. Reproduction or use for any purpose other than that authorized by Stantec is forbidden.

Consultants

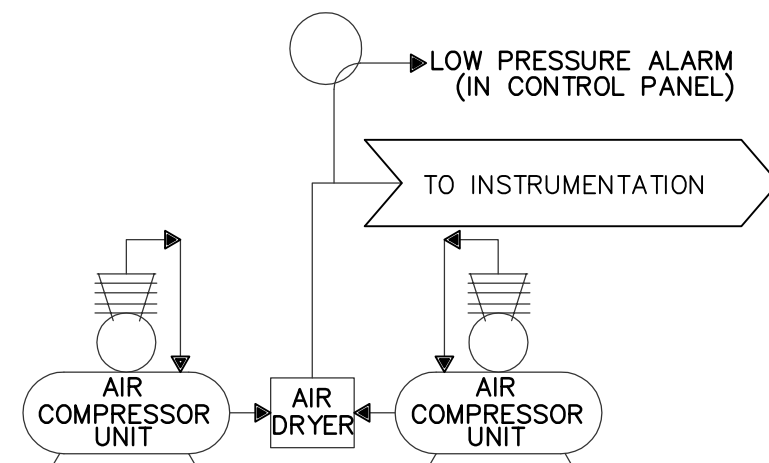

Revision	By	Appd.	YY.MM.DD
MDEQ PERMIT	WA	IMN	07.03.02
Issued	By	Appd.	YY.MM.DD

File Name: 0P1-03 ProcessFlow.dwg	JLP	IMN	WA	
	Dwn.	Chkd.	Dsgn.	YY.MM.DD

Permit-Seal

Client/Project

CITY OF CADILLAC, MICHIGAN
WASTEWATER TREATMENT PLANT
2007 IMPROVEMENTS

CADILLAC, MI

Title
PROCESS FLOW
DIAGRAM III

Project No. 2075006103	Scale AS NOTED	
Drawing No.	Sheet	Revision

0P1.03 of

Of