

From: Brady, Donal (DEQ)
Sent: 7/25/2018 5:41:35 PM
To: "Popovich, Bradley (DEQ)" <PopovichB@michigan.gov>
Subject: FW: Cadillac WWTP - Past Correspondence Inquiry
Attachments: Process Flow Diagram.pdf

Hi Bradley,

I missed this email. The City revised page 1 of the flow diagram. Please see the attached. Pages 2 and 3 of the diagram (previously submitted) should be representative. Sorry about this.



Don Brady, P.E.
Michigan Department of Environmental Quality
Water Resources Division
Cadillac District Office
120 West Chapin Street
Cadillac, MI 49601
BradyD6@michigan.gov
(231) 876-4478

From: Doug Langworthy <dlangworthy@Cadillac-MI.net>
Sent: Wednesday, June 20, 2018 10:47 AM
To: Brady, Donal (DEQ) <BradyD6@michigan.gov>
Subject: RE: Cadillac WWTP - Past Correspondence Inquiry

Don,
This is the most current process flow diagram I have.
Doug

Douglas Langworthy
Assistant Water Resources Supervisor
City of Cadillac
231-775-2841

From: Brady, Donal (DEQ) [<mailto:BradyD6@michigan.gov>]
Sent: Wednesday, June 20, 2018 9:14 AM
To: Doug Langworthy
Subject: FW: Cadillac WWTP - Past Correspondence Inquiry

Hi Doug,

Our permit staff is asking for an updated process flow diagram for the plant. Do you know if an updated diagram was prepared and if so could you send it to me? Is the only change the UV vs. chlorine for disinfection?

P.S. I am still working on the paperwork from our inspection. Hope to send you something next week.



Don Brady, P.E.
Michigan Department of Environmental Quality
Water Resources Division
Cadillac District Office
120 West Chapin Street
Cadillac, MI 49601
BradyD6@michigan.gov
(231) 876-4478

From: Brady, Donal (DEQ)
Sent: Wednesday, June 20, 2018 9:11 AM
To: Popovich, Bradley (DEQ) <PopovichB@michigan.gov>
Subject: RE: Cadillac WWTP - Past Correspondence Inquiry

Hi Bradley,

Sorry for the delayed response. I am relatively new at the DEQ (started Jan 2017) and don't think I was around for the conversation about the WWTP flow diagram. I don't believe an updated flow diagram has been submitted to the DEQ. I have asked the City about this. I know the WWTP now uses UV for disinfection, think that might be the only change in the flow diagram. What is the brochure?

The flow diagrams I have seen are attached.



Don Brady, P.E.
Michigan Department of Environmental Quality
Water Resources Division
Cadillac District Office
120 West Chapin Street
Cadillac, MI 49601
BradyD6@michigan.gov
(231) 876-4478

From: Popovich, Bradley (DEQ)
Sent: Thursday, June 14, 2018 1:16 PM
To: Brady, Donal (DEQ) <BradyD6@michigan.gov>
Subject: Cadillac WWTP - Past Correspondence Inquiry

Good Afternoon Donal,

I am currently working on the reissuance of Cadillac WWTP's IP and found mention, within the biologist Fact Sheet (Item 5), of an email asking the facility to update their flow diagram and brochure. Has the permittee provided this information? And, if possible, could you please forward me that email conversation so that I can upload it to the record. Thank you very much for your time.

Sincere regards,

Bradley Popovich

Environmental Quality Analyst

Water Resources Division

Municipal Permits Unit

Michigan Department of Environmental Quality

(517) 284-6656

PopovichB@Michigan.gov

Monday – Friday 8:00-4:30

ATTACHMENT NAME:

Process Flow Diagram.pdf

ATTACHMENT TYPE:

Adobe Portable Document Format (PDF) compound image




Stantec Consulting Michigan Inc.
3959 Research Park Drive
Ann Arbor, Michigan
48108-2216
Tel. 734.761.1010
Fax. 734.761.1200
www.stantec.com

Stantec

Copyright Reserved

The Contractor shall verify and be responsible for all dimensions. DO NOT scale the drawing - any errors or omissions shall be reported to Stantec without delay.
The Copyrights to all designs and drawings are the property of Stantec. Reproduction or use for any purpose other than that authorized by Stantec is forbidden.

Consultants

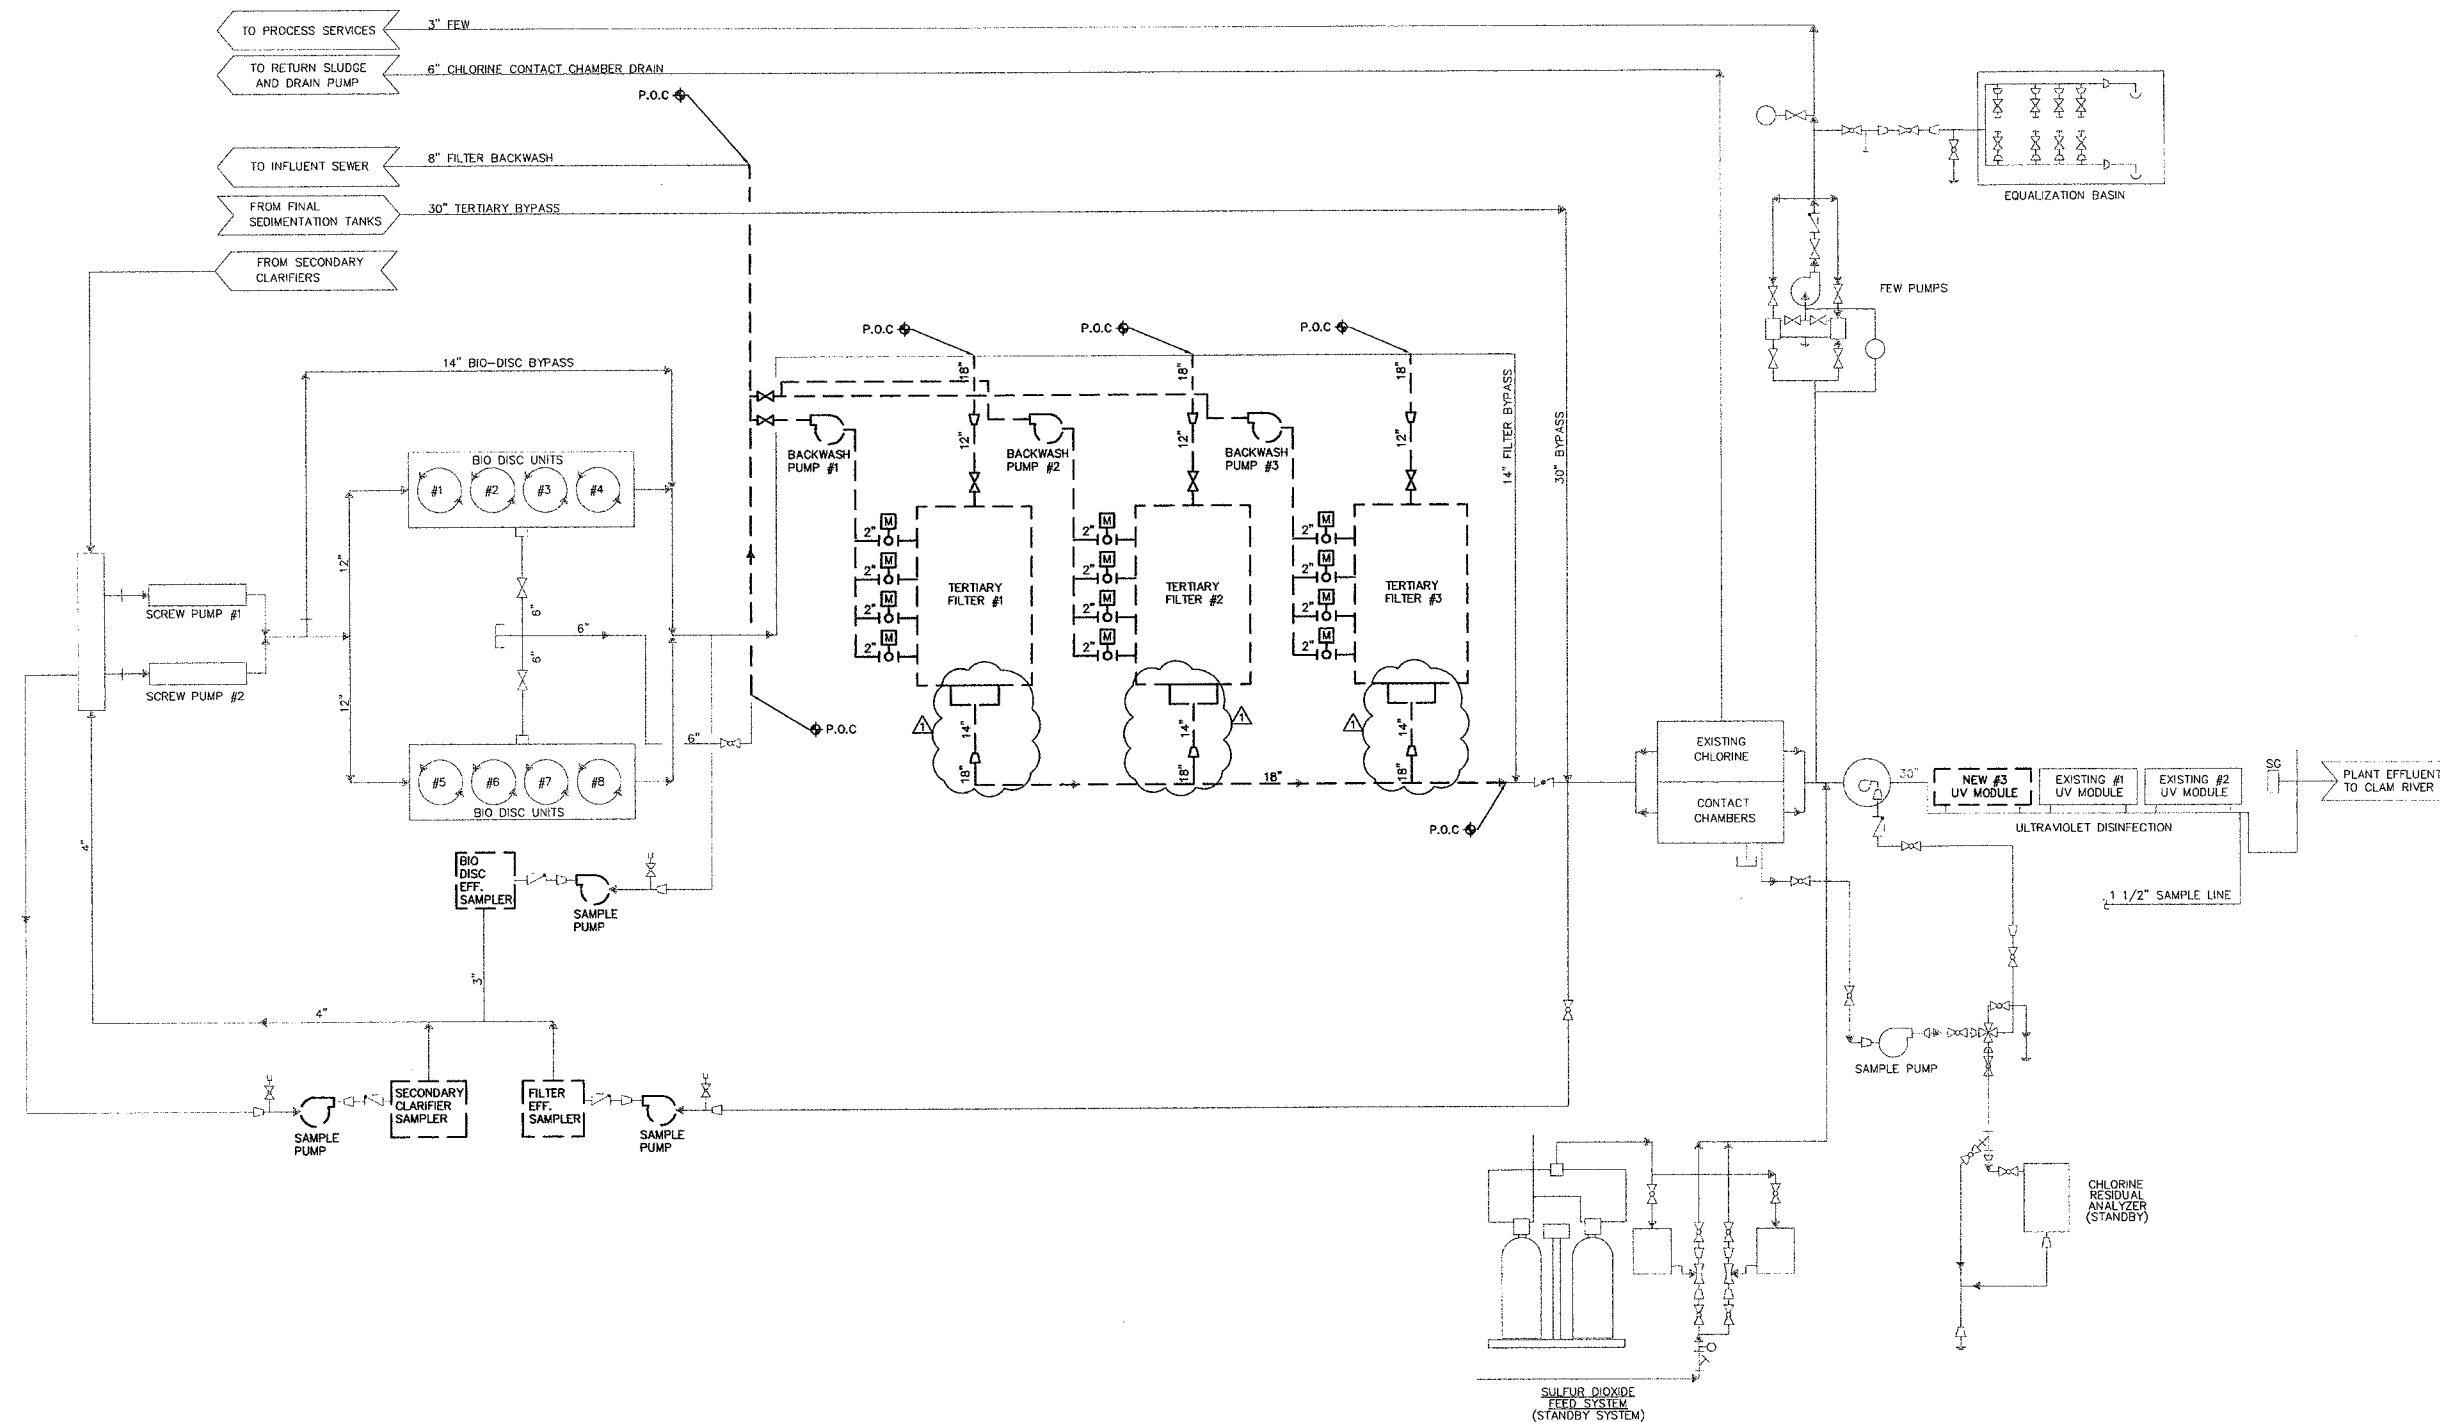

LEGEND

- NEW
- EXISTING
- ◆ P.O.C POINT OF CONNECTION

Revision	By	Appd.	YY.MM.DD
CONSTRUCTION SET	WA	IMN	07.11.09
ADDENDUM #1	WA	IMN	07.07.13
BID SET	WA	IMN	07.06.22
FINAL REVIEW SET	WA	IMN	07.05.15
DRAFT REVIEW SET	WA	IMN	07.03.02
Issued	By	Appd.	YY.MM.DD

File Name: GP1-01 ProcessFlow	JLP	IMN	WA
	Dwn.	Chkd.	Dsgn.
Permit-Seal			YY.MM.DD

Client/Project
CITY OF CADILLAC, MICHIGAN
2007 WASTEWATER TREATMENT PLANT
AND COLLECTION SYSTEM
IMPROVEMENTS
CADILLAC, MI

Title
PROCESS FLOW
DIAGRAM III

Project No.
2075006103

Drawing No.

OP1.03